

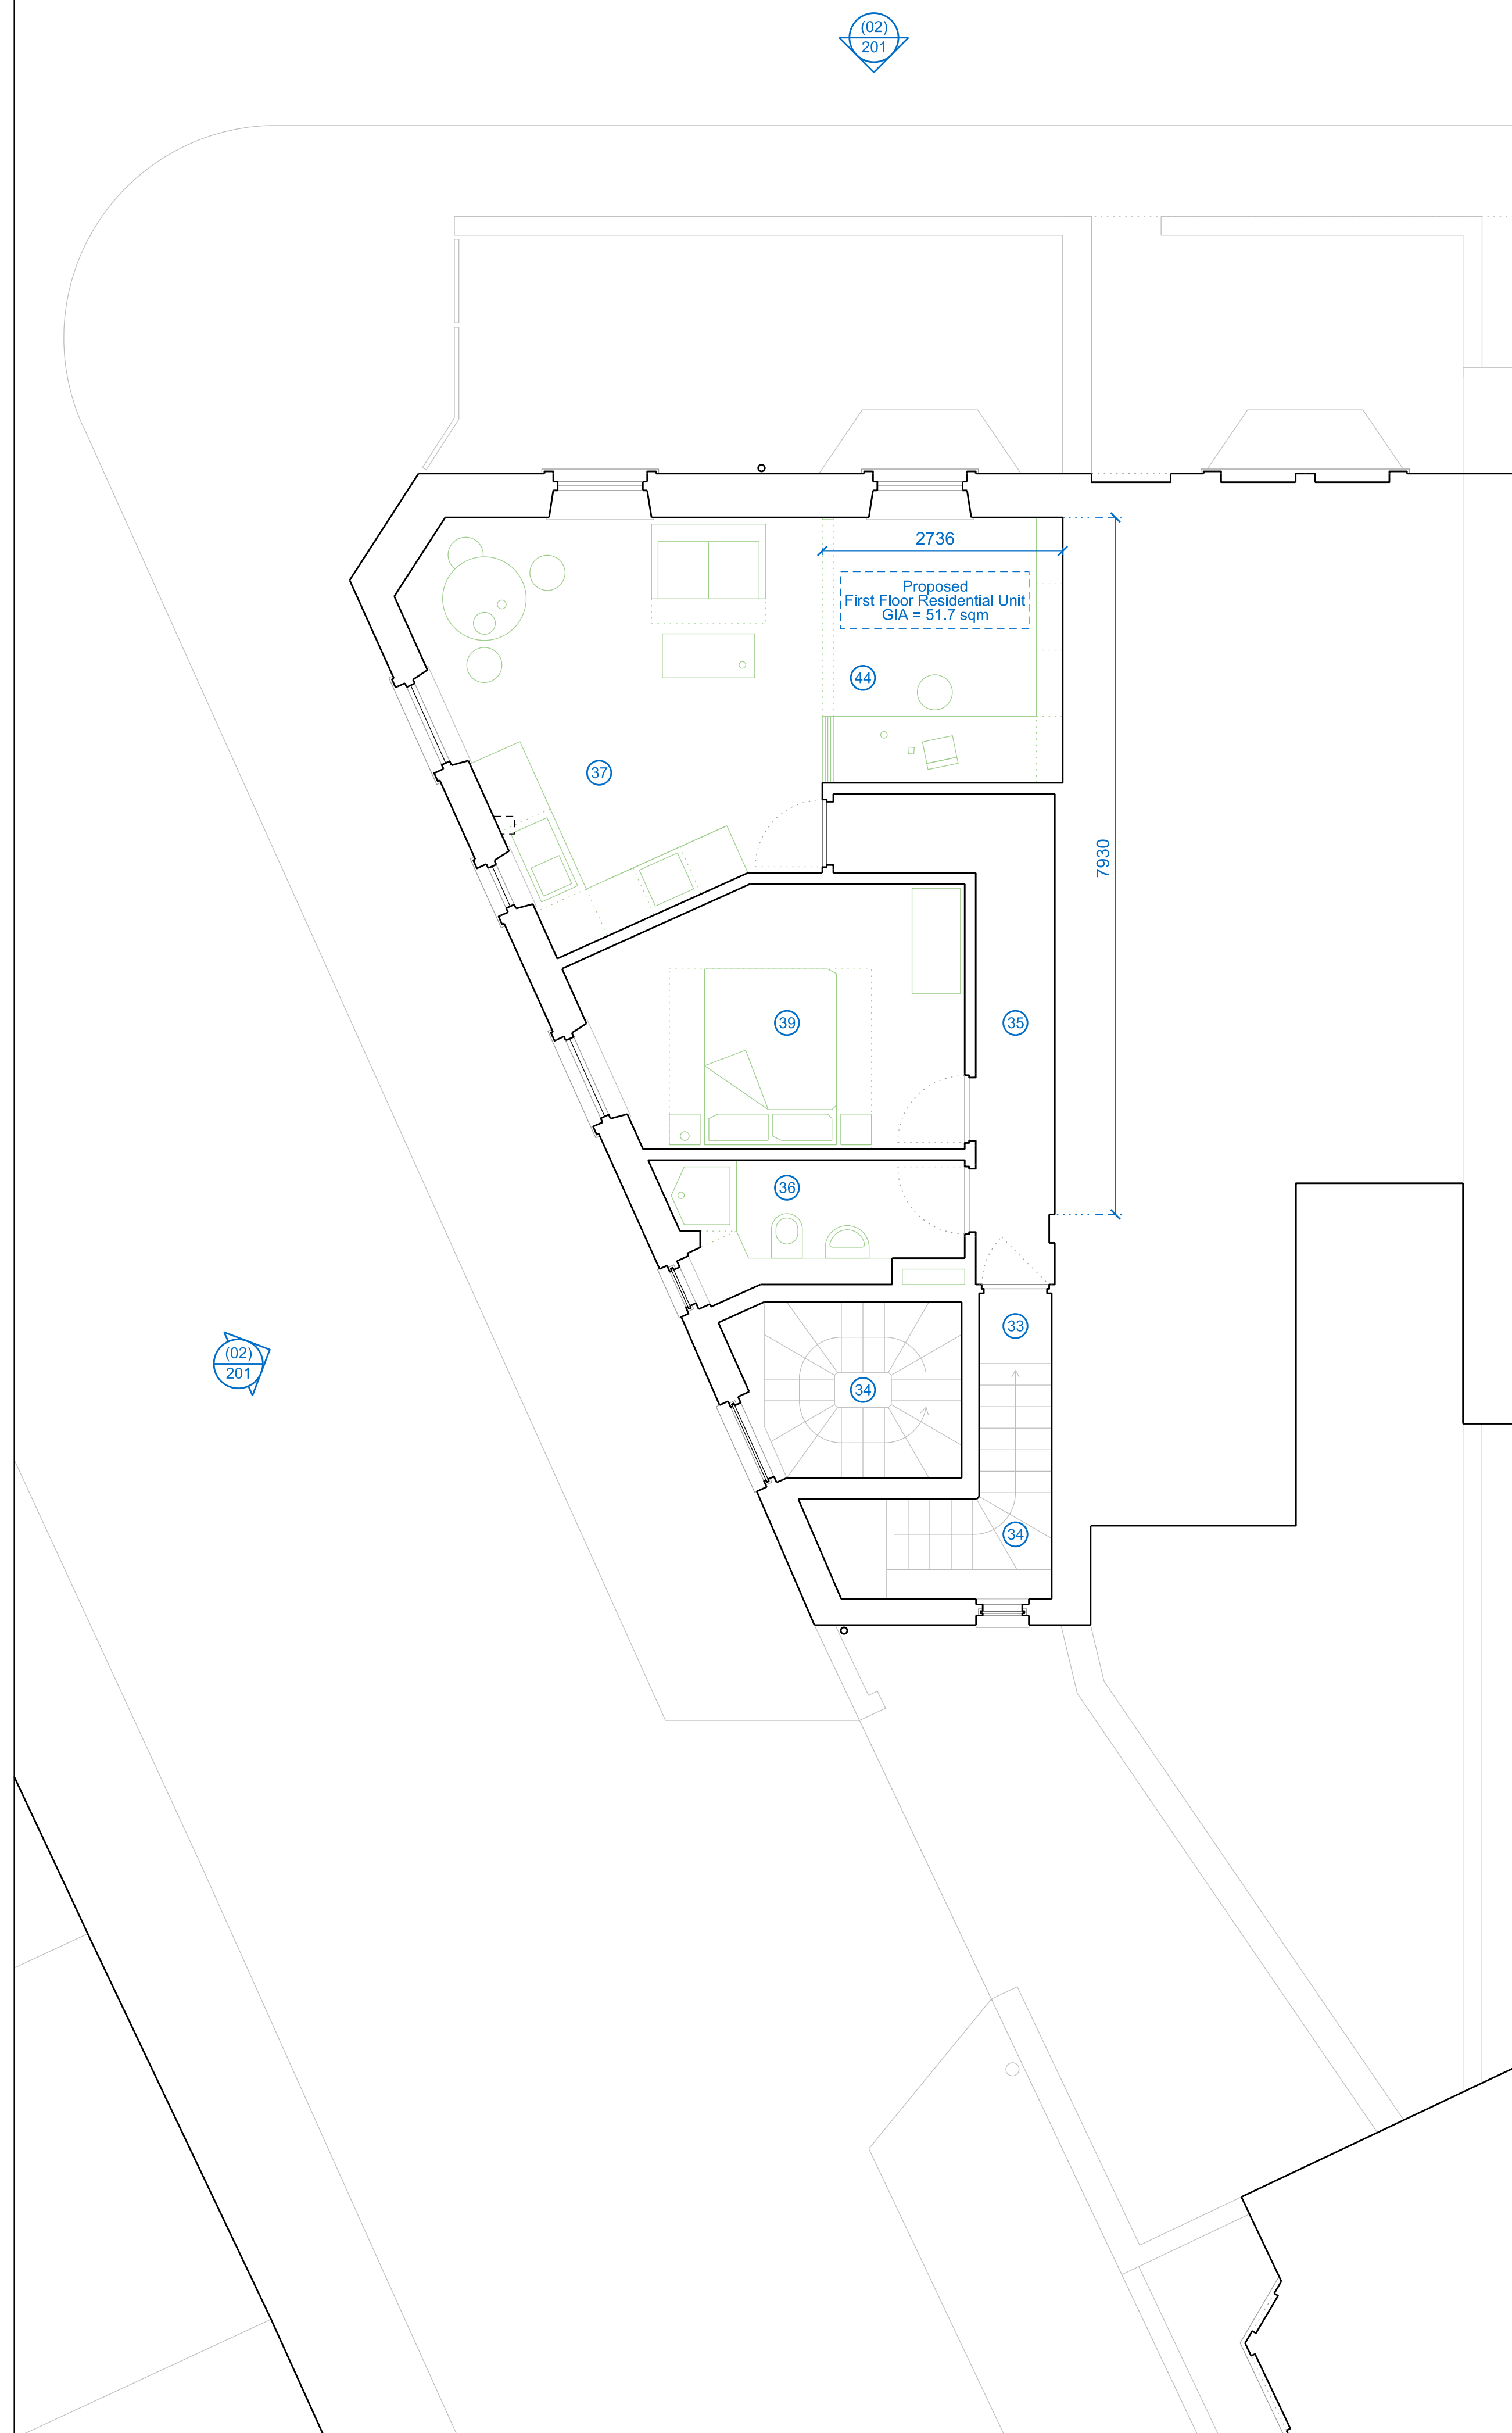


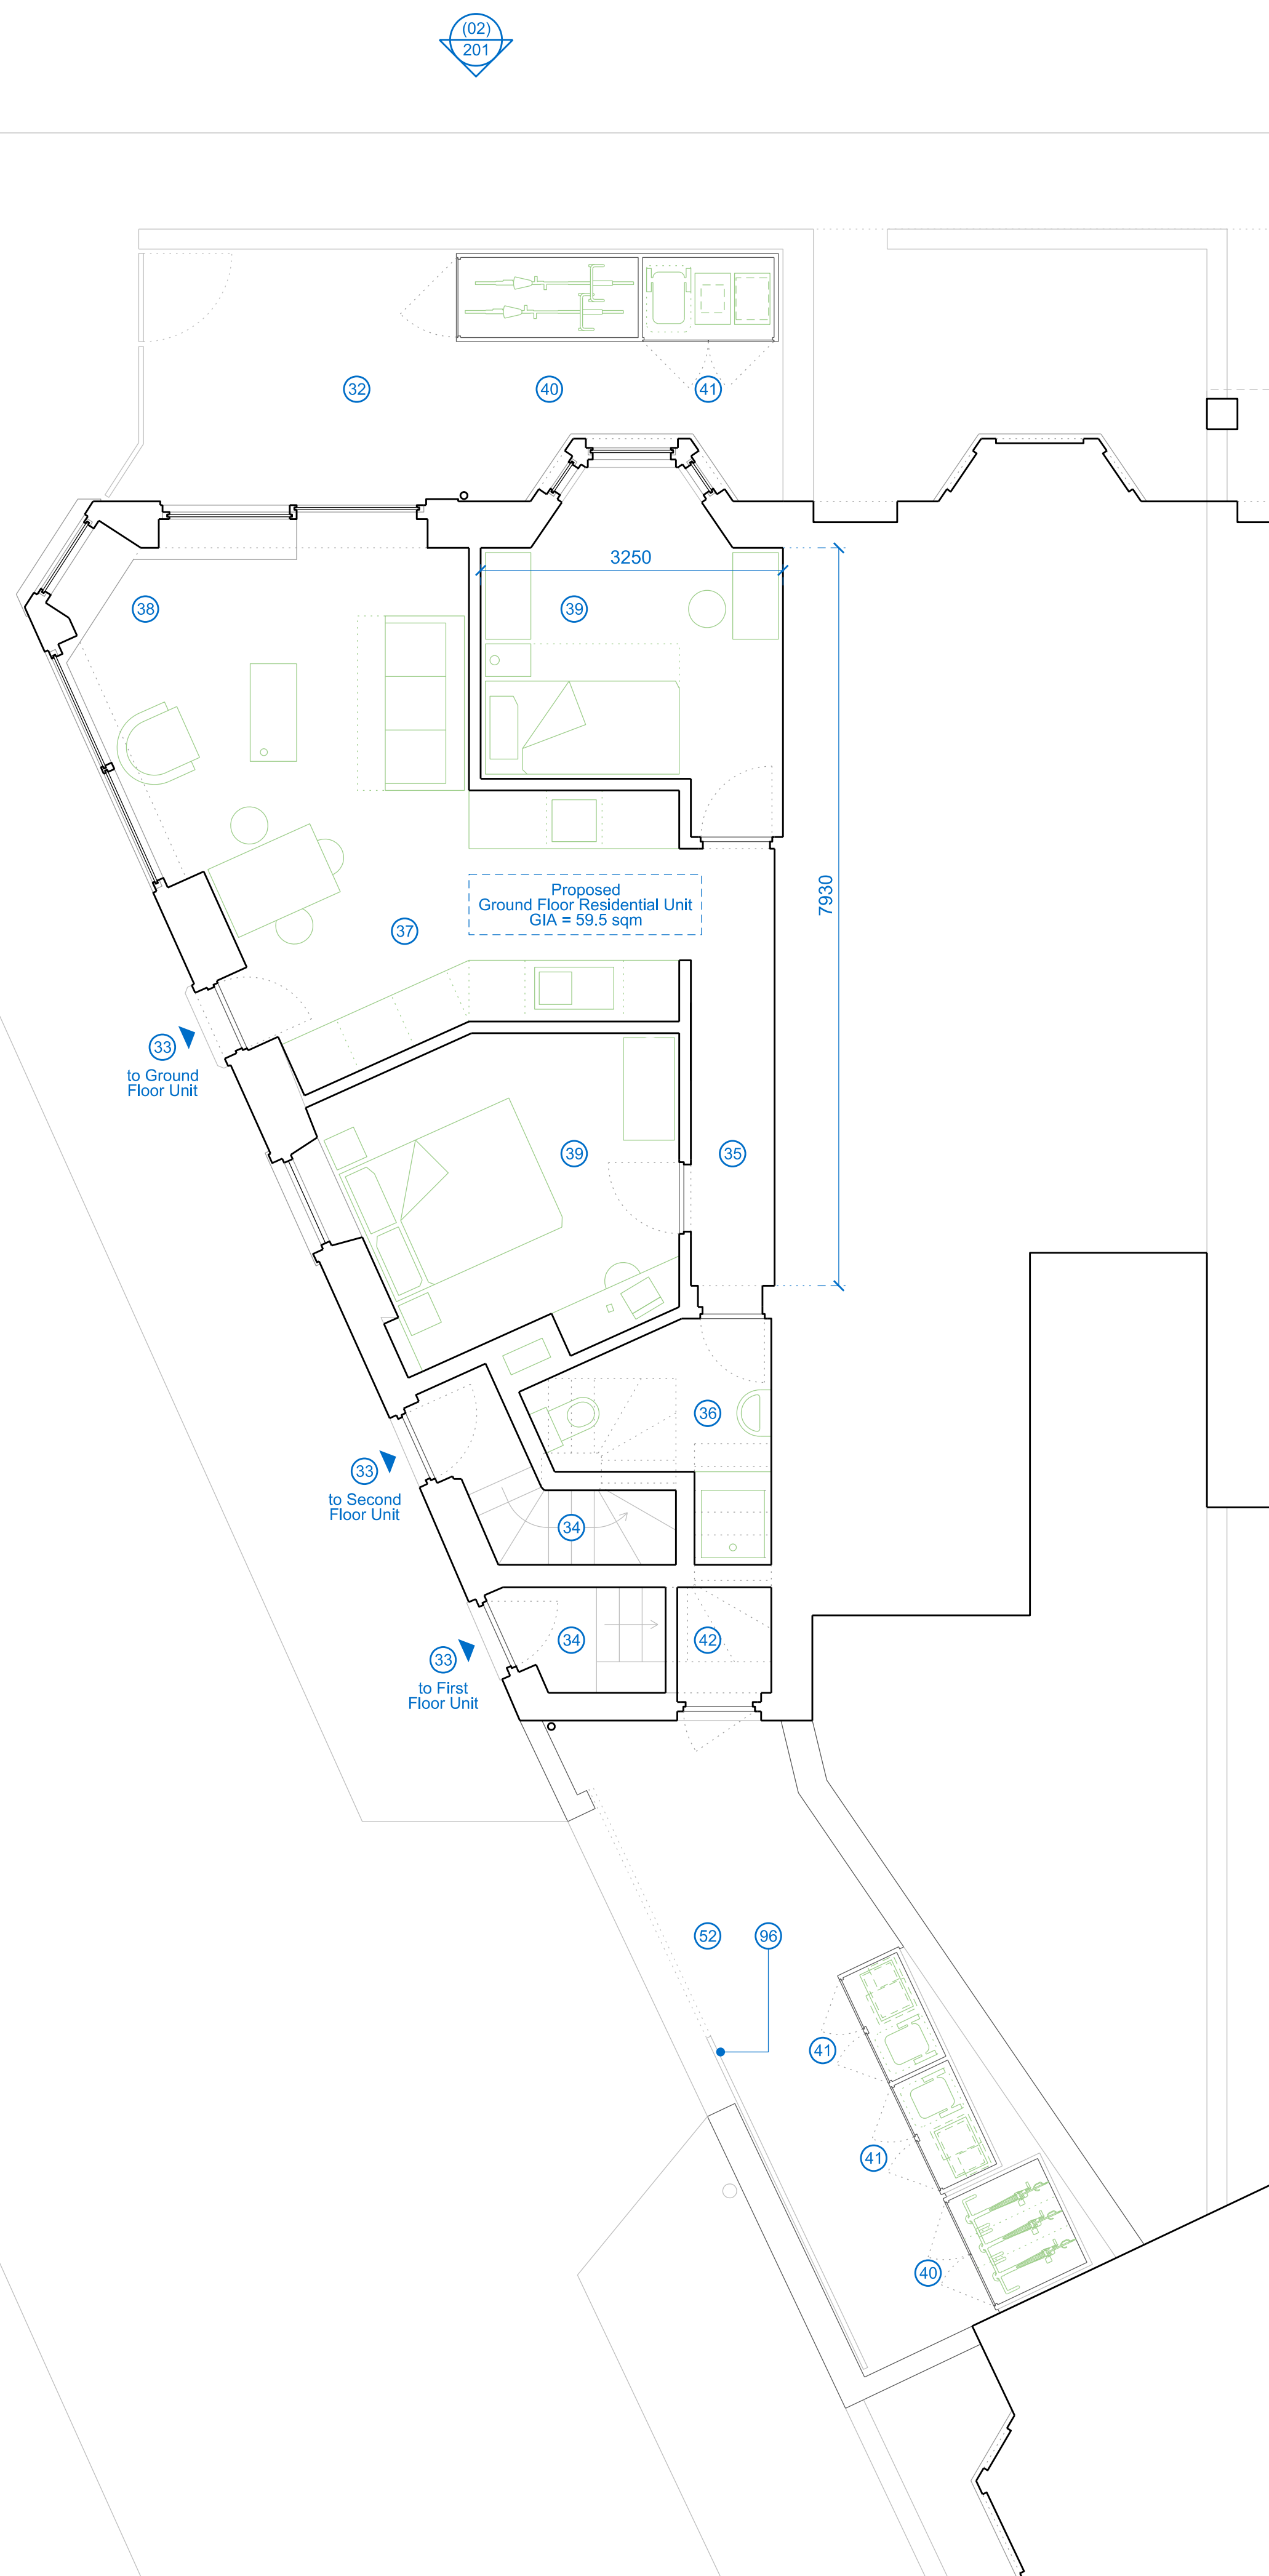

|                 |                                                                                        |
|-----------------|----------------------------------------------------------------------------------------|
| KEY             |                                                                                        |
| EXISTING SPACES |                                                                                        |
| 01              | Commercial                                                                             |
| 02              | Entrance                                                                               |
| 03              | Shop                                                                                   |
| 04              | Back of house                                                                          |
|                 | WC                                                                                     |
|                 | Residential                                                                            |
| 06              | Entrance                                                                               |
| 07              | Stair                                                                                  |
| 08              | Hall                                                                                   |
| 09              | Bathroom                                                                               |
| 10              | Kitchen                                                                                |
| 11              | Living space                                                                           |
| 12              | Bedroom                                                                                |
|                 | Other                                                                                  |
| 16              | Forecourt                                                                              |
| 17              | Parking space                                                                          |
| PROPOSED SPACES |                                                                                        |
| 32              | Front garden                                                                           |
| 33              | Entrance                                                                               |
| 34              | Stair                                                                                  |
| 35              | Hall                                                                                   |
| 36              | Bathroom                                                                               |
| 37              | Kitchen                                                                                |
| 38              | Living space                                                                           |
| 39              | Bedroom                                                                                |
| 40              | Cycle store                                                                            |
| 41              | Refuse store                                                                           |
| 42              | Built-in storage                                                                       |
| 43              | Utility room                                                                           |
| 44              | Study                                                                                  |
| EXISTING FABRIC |                                                                                        |
|                 | Landscape                                                                              |
| 51              | Cracked concrete surface                                                               |
| 52              | Asphalt surface                                                                        |
| 53              | Dropped kerb                                                                           |
|                 | Elevations                                                                             |
| 55              | Rendered boundary wall & timber trellis                                                |
| 56              | Stone masonry                                                                          |
| 57              | Rendered architrave / quoin                                                            |
| 58              | Textured rendered wall / stallriser                                                    |
| 59              | Brick masonry                                                                          |
| 60              | Black uPVC rainwater goods                                                             |
| 61              | uPVC-framed double-glazed window / door                                                |
| 62              | Aluminium-framed shopfront                                                             |
| 63              | Security shutter metal housing                                                         |
| 64              | Metal signage                                                                          |
| 65              | Blocked up opening                                                                     |
| 66              | Concrete roof tile                                                                     |
| 67              | Felt flat-roof                                                                         |
| 68              | Boarded door                                                                           |
| 69              | Concrete render                                                                        |
| 70              | Air-conditioning unit                                                                  |
| PROPOSED FABRIC |                                                                                        |
|                 | Landscape                                                                              |
| 71              | New paving                                                                             |
| 72              | New rendered boundary wall and copings<br>with painted metal railings and gate to side |
|                 | Elevations                                                                             |
| 81              | Rendered wall                                                                          |
| 82              | Tiled stallriser                                                                       |
| 83              | uPVC conservation-style window / door                                                  |
| 85              | Period-style timber shopfront<br>with aluminium-framed double-glazing                  |
| 86              | Painted timber signage board                                                           |
| 87              | Black cast-iron-style uPVC rainwater goods                                             |
| 88              | Concrete roof tile - to match existing                                                 |
| 89              | Conservation-style Velux rooflight                                                     |
| 90              | Lead dormer cheeks / roof                                                              |
| 91              | Dark grey single-ply flat-roof membrane                                                |
| 93              | Painted timber door                                                                    |
| 94              | Painted render to match existing features                                              |
| 95              | Air-source heat pump                                                                   |
| 96              | Gate                                                                                   |
| 97              | Trellis                                                                                |

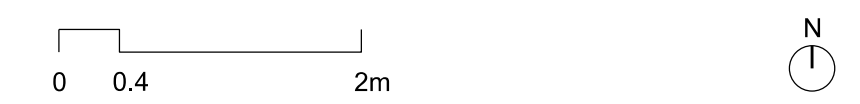

|             |                                |                |          |   |
|-------------|--------------------------------|----------------|----------|---|
| job         | REDFIELD                       |                |          | <small>           Do not scale from this drawing.<br/>           All items to be checked on this by the Contractor<br/>           and dimensions are to be true (unrounded).<br/>           All dimensions are in non-units noted         </small> |
| drawing     | PROPOSED PLANS : GF + 1F PLANS |                |          |   |
| status      | PLANNING                       |                |          |   |
| scale       | 1:50                           | at A1          | 1:100    | at A3   |
| job nr.     | source                         | drawing number | revision |   |
| <b>A092</b> | <b>A</b>                       | <b>(02)101</b> | <b>A</b> |   |